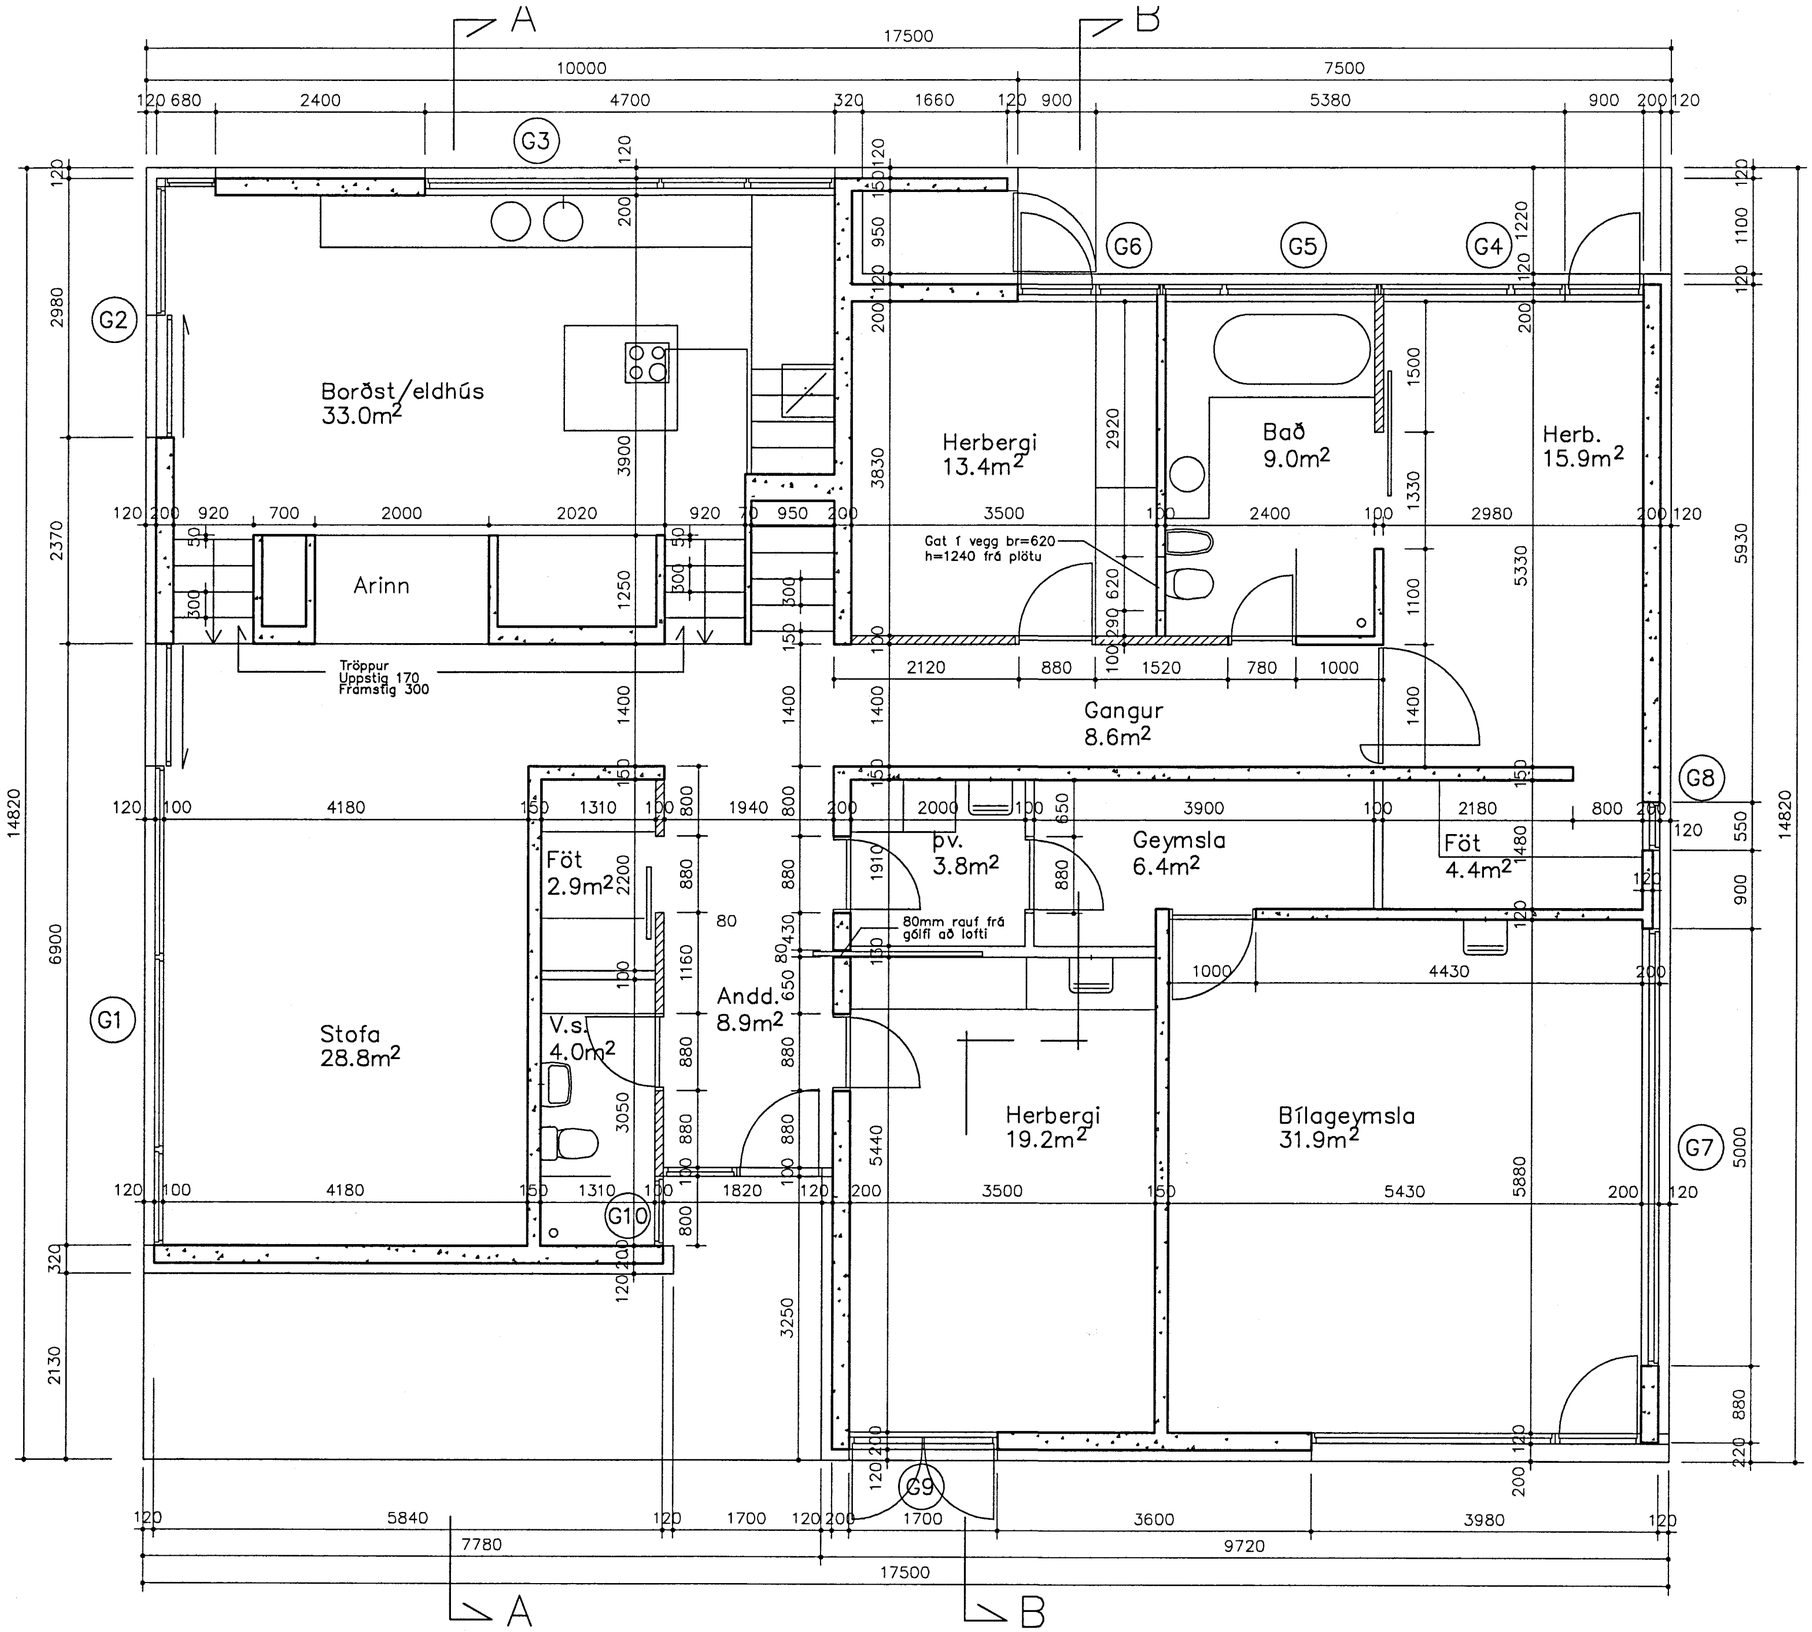

Grunnmynd mkv.1:50

Notkun teikningar leyfð
á ábyrgð höfundar
29 JÚNÍ 2000
byggingarfulltrúinn

185287

JÖKLALIND 5 KÓPAVOGI

GRUNNMYND 1.HÆÐAR 1:50
18.04.2000 NR 1.01

ÁSMUNDUR H. STURLUSON
280865-2959 ARKITEKT FAÍ
BJARNI SNÆBJÖRNSSON
020753-4989 ARKITEKT FAÍ
LAUGARNESVEGUR 96 105 REYKJAVÍK 588 3811